# HomePlan — Ground floor (1 of 2)

Footprint: 50' x 38.5' · Total: 1687.6 sqft · 8 rooms

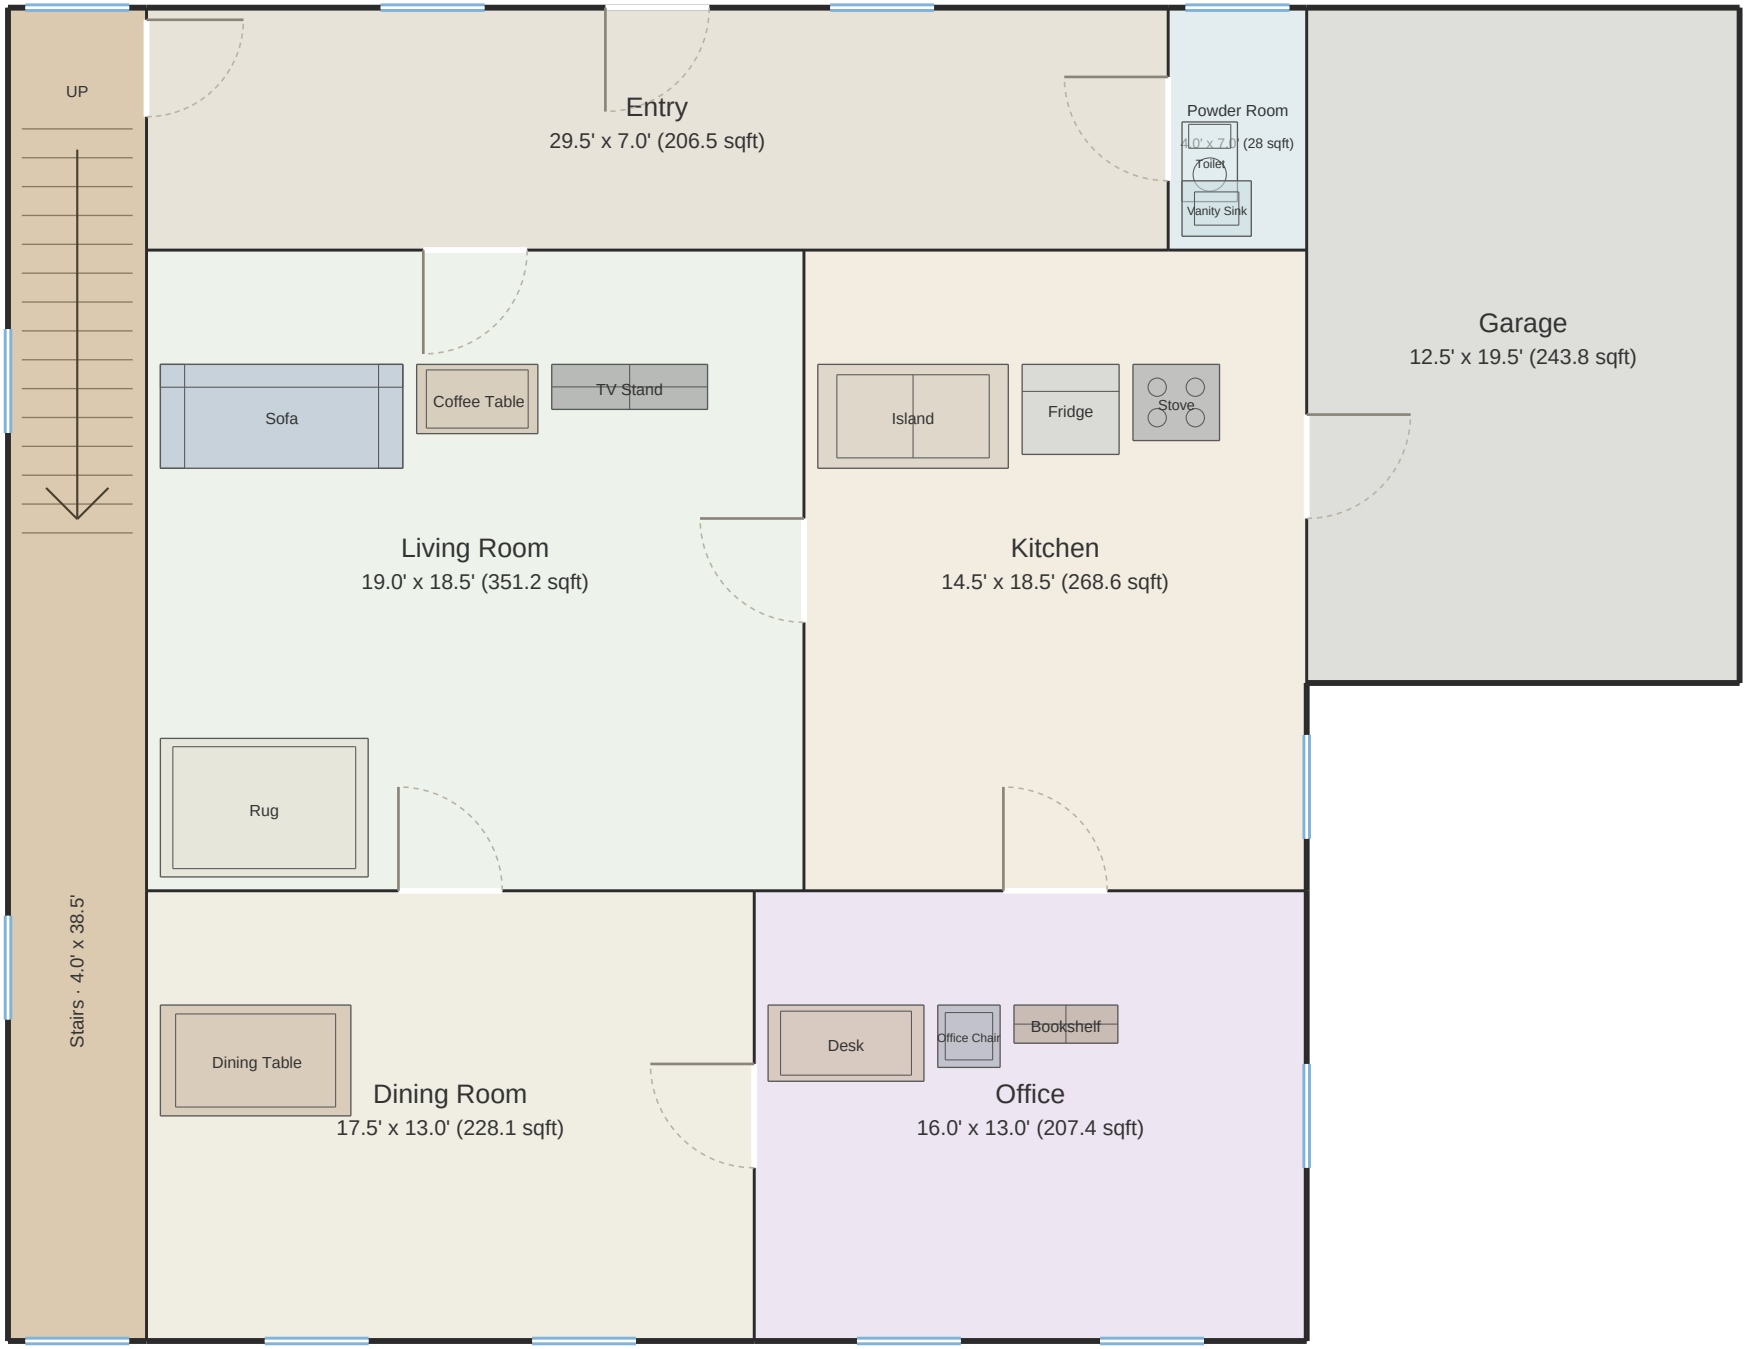

# HomePlan — Upper floor (2 of 2)
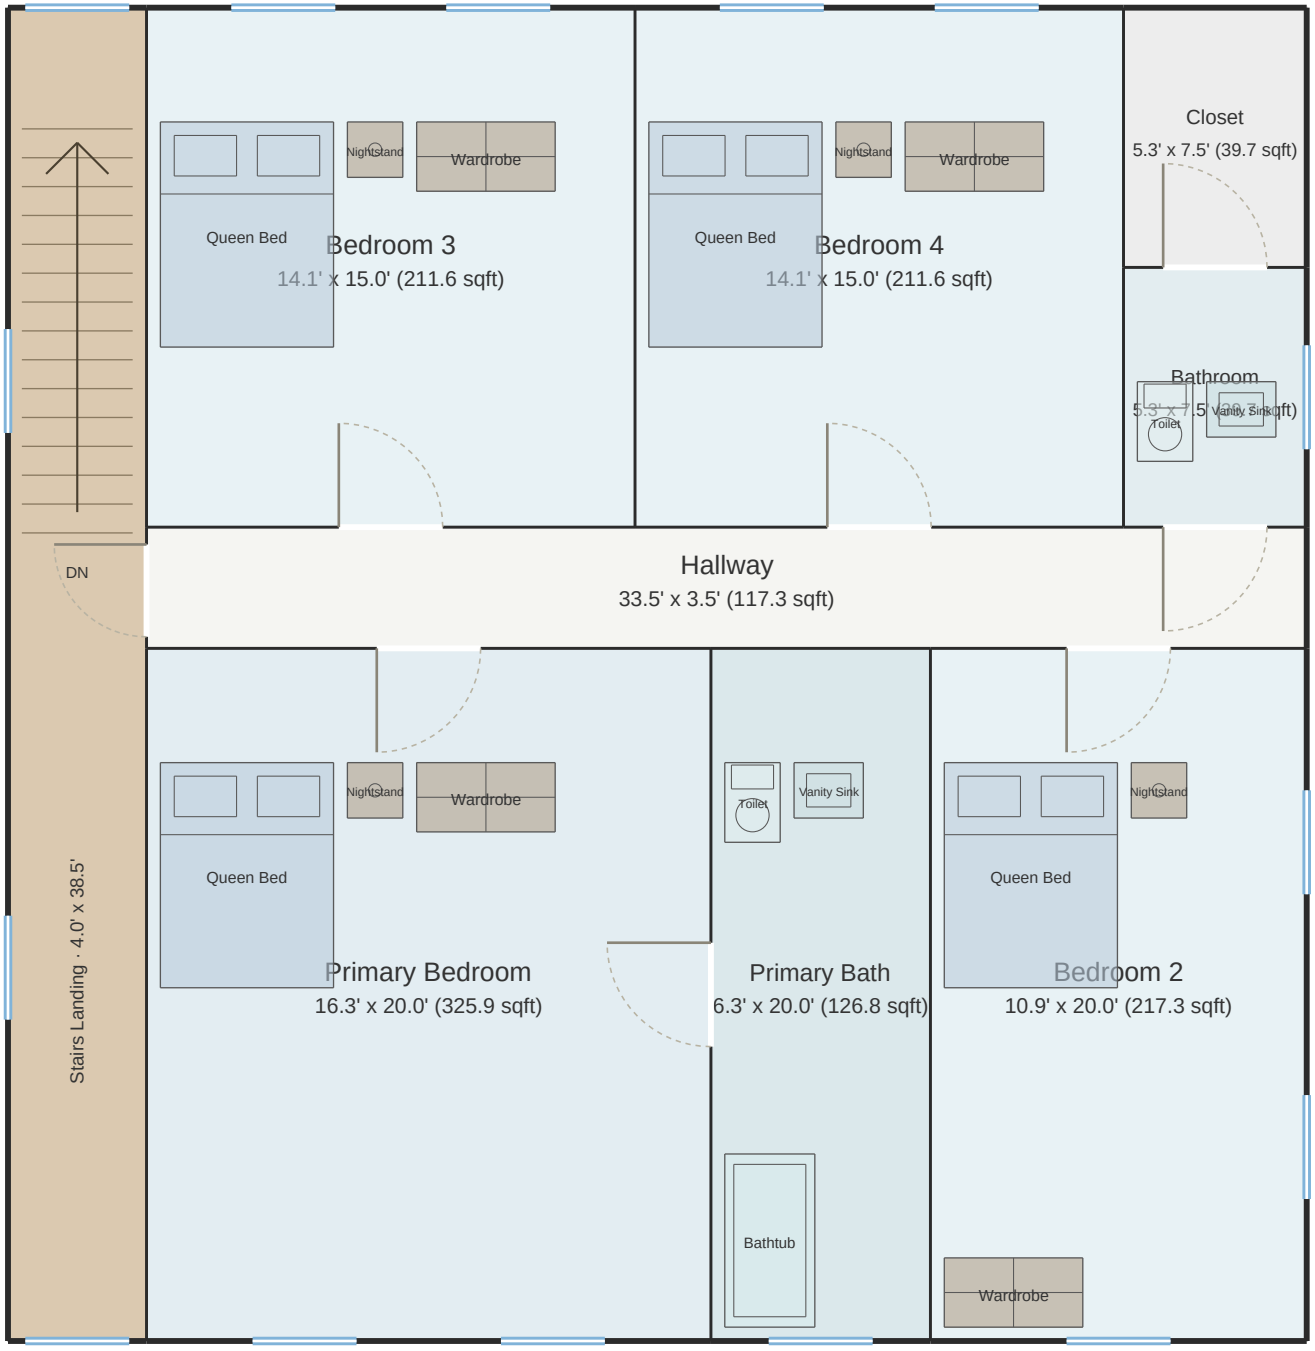
Footprint: 50' x 38.5' · Total: 1443.9 sqft · 9 rooms